
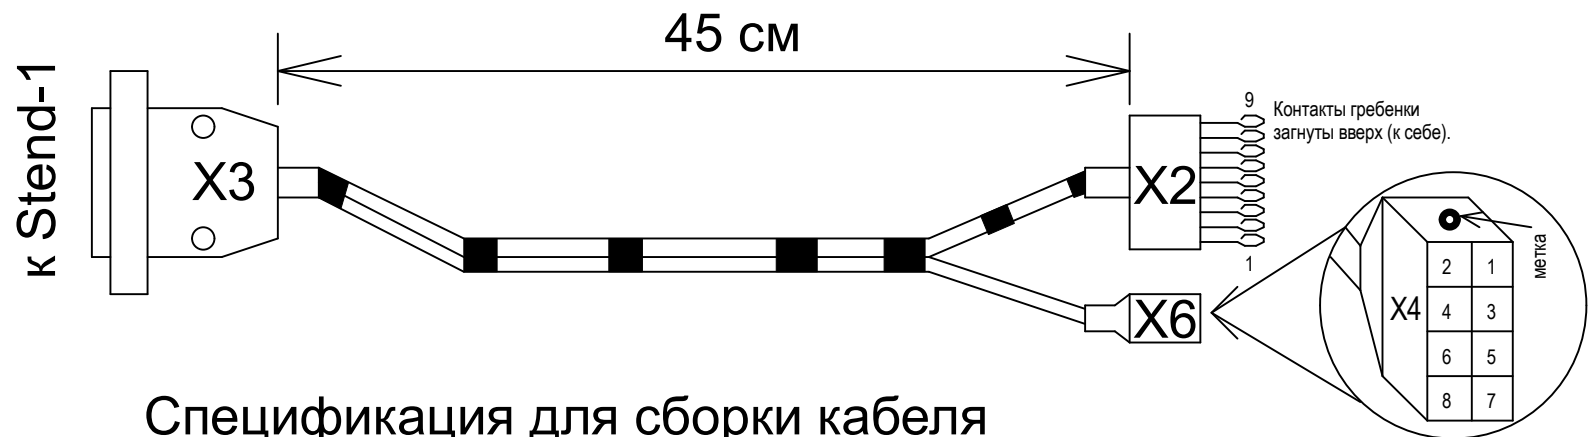


Схема кабеля для подключения STEND-1 к (161,193,201,206) Z-5R Wiegand

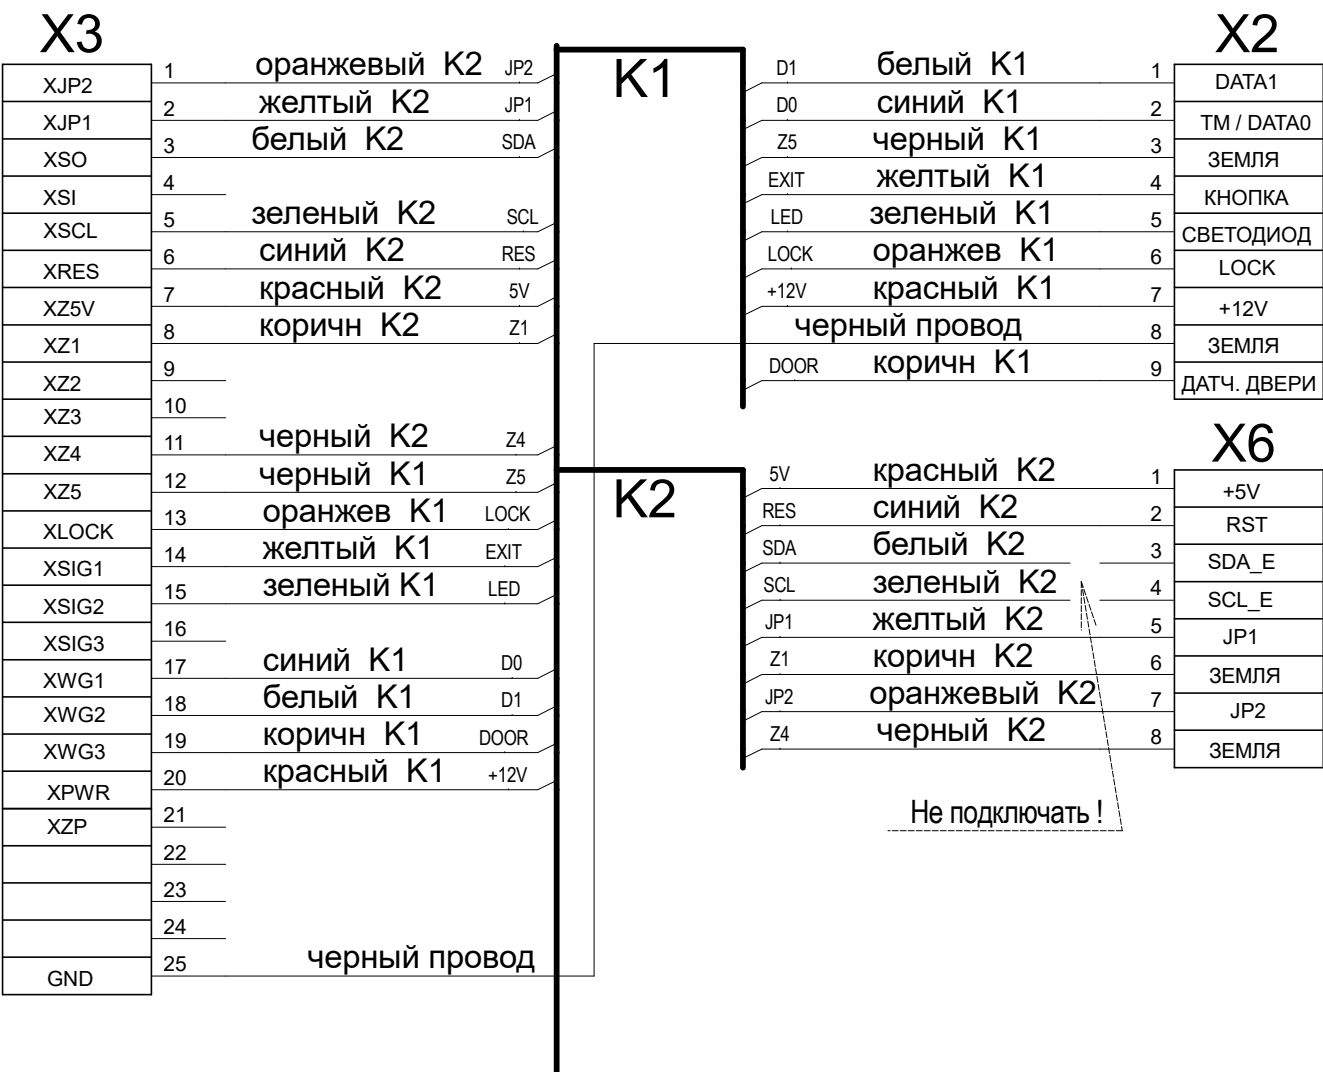

Спецификация для сборки кабеля

RefDes	Наименование
X2	гребенка 9 конт.
X3	DB-25 (папа)
X6	BLD 2x4 - 1 шт контакт BLS - 8 шт
K1	CAB-8 50 см
K2	CAB-8 50 см